NORTH WEST

NORTH

NORTH EAST

84'-6"

PARENT'S BEDROOM

19'-5"

12'-6"

LIVING

DINING AREA

DECK

LAWN

8'-5"
SHOWER

PARENT'S
BATHROOM

PARENT'S
WARDROBE

5'-3"

9'-8"

ENTRY
PORCH

FOYER

ROAD

MH

CH

WEST

43'

28'

UP

5'-8"

10'-7"

KITCHEN

PARKING

UP

STUDY ROOM

11'-10"

11'

POWDER
ROOM

7'-3"

6'-2"

COMMUNICATION
ROOM

UTILITY

16'-3"

LIFT

4'


84'-4"

SOUTH WEST


SOUTH

SOUTH EAST

PROJECT :	SHEET TITLE :	PARTICULARS	BY	SCALE :	DATE :	DESIGN CONSULTANT :
FLORESTA 28	**GROUND FLOOR PLAN**	DRAWN :-	OM	N.T.S.	03-07-2026	**ICONIC DESIGN INDIA**
MR. MANIK'S RESIDENCE		CHECKED :-	SB	PAPER SIZE :	SHEET NO : FR-CD-F01	EAST SAPPHIRE , SECTOR - 45 NOIDA(U.P.)201301
		REVISION :-	R4			

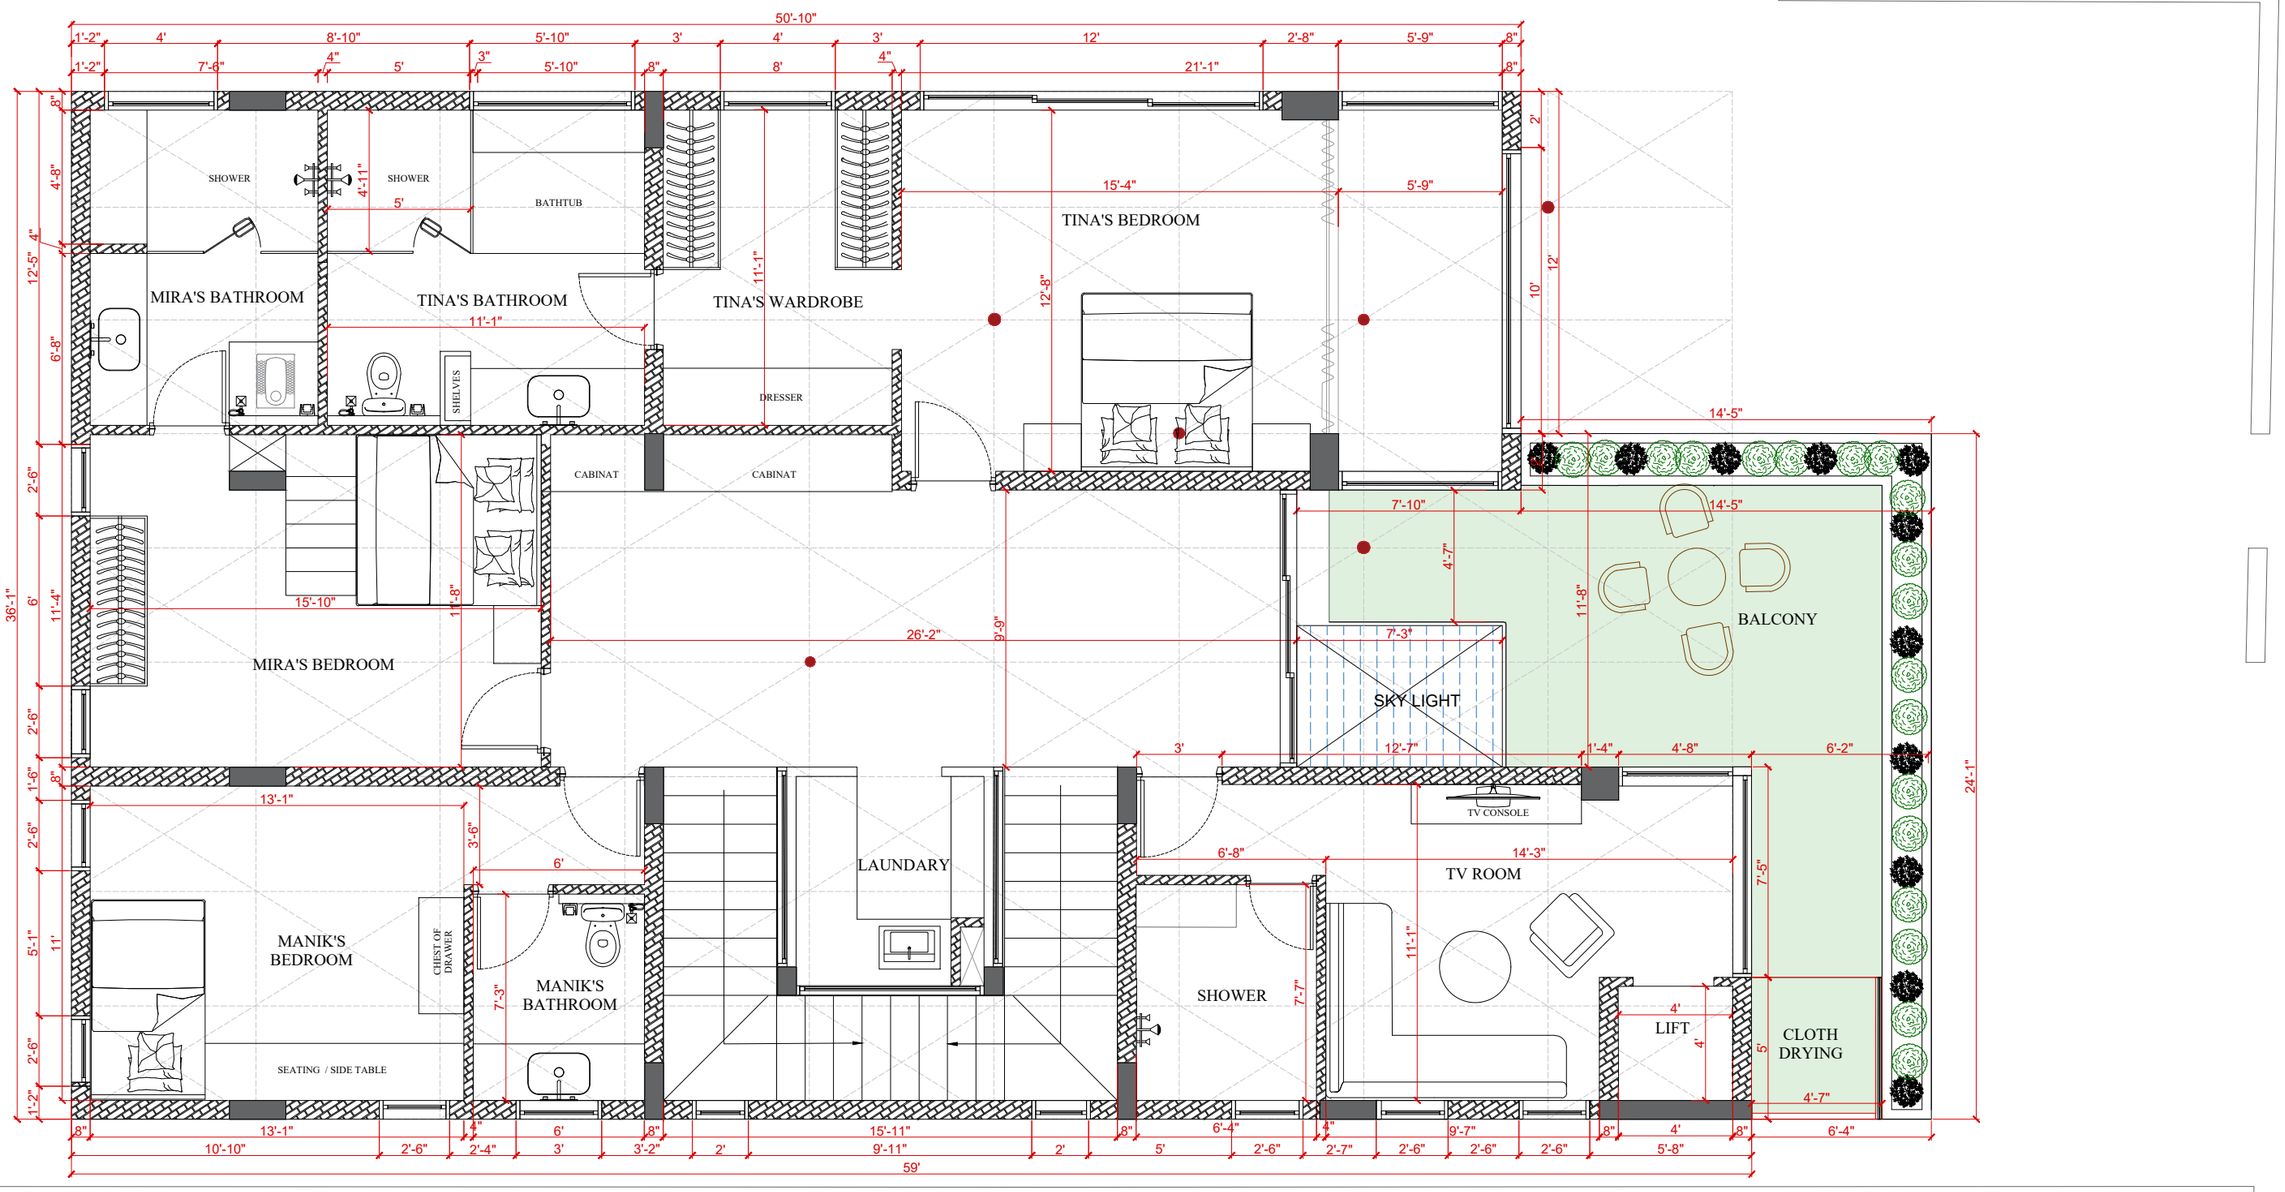


PROJECT : FLORESTA 28 — MR. MANIK'S RESIDENCE	SHEET TITLE : **FIRST FLOOR PLAN**	PARTICULARS / BY: DRAWN :- OM; CHECKED :- SB; REVISION :- R5	SCALE : N.T.S. — PAPER SIZE :	DATE : 03-07-2026 — SHEET NO : FR-CD-F02	DESIGN CONSULTANT : **ICONIC DESIGN INDIA** EAST SAPPHIRE , SECTOR - 45 NOIDA(U.P.)201301

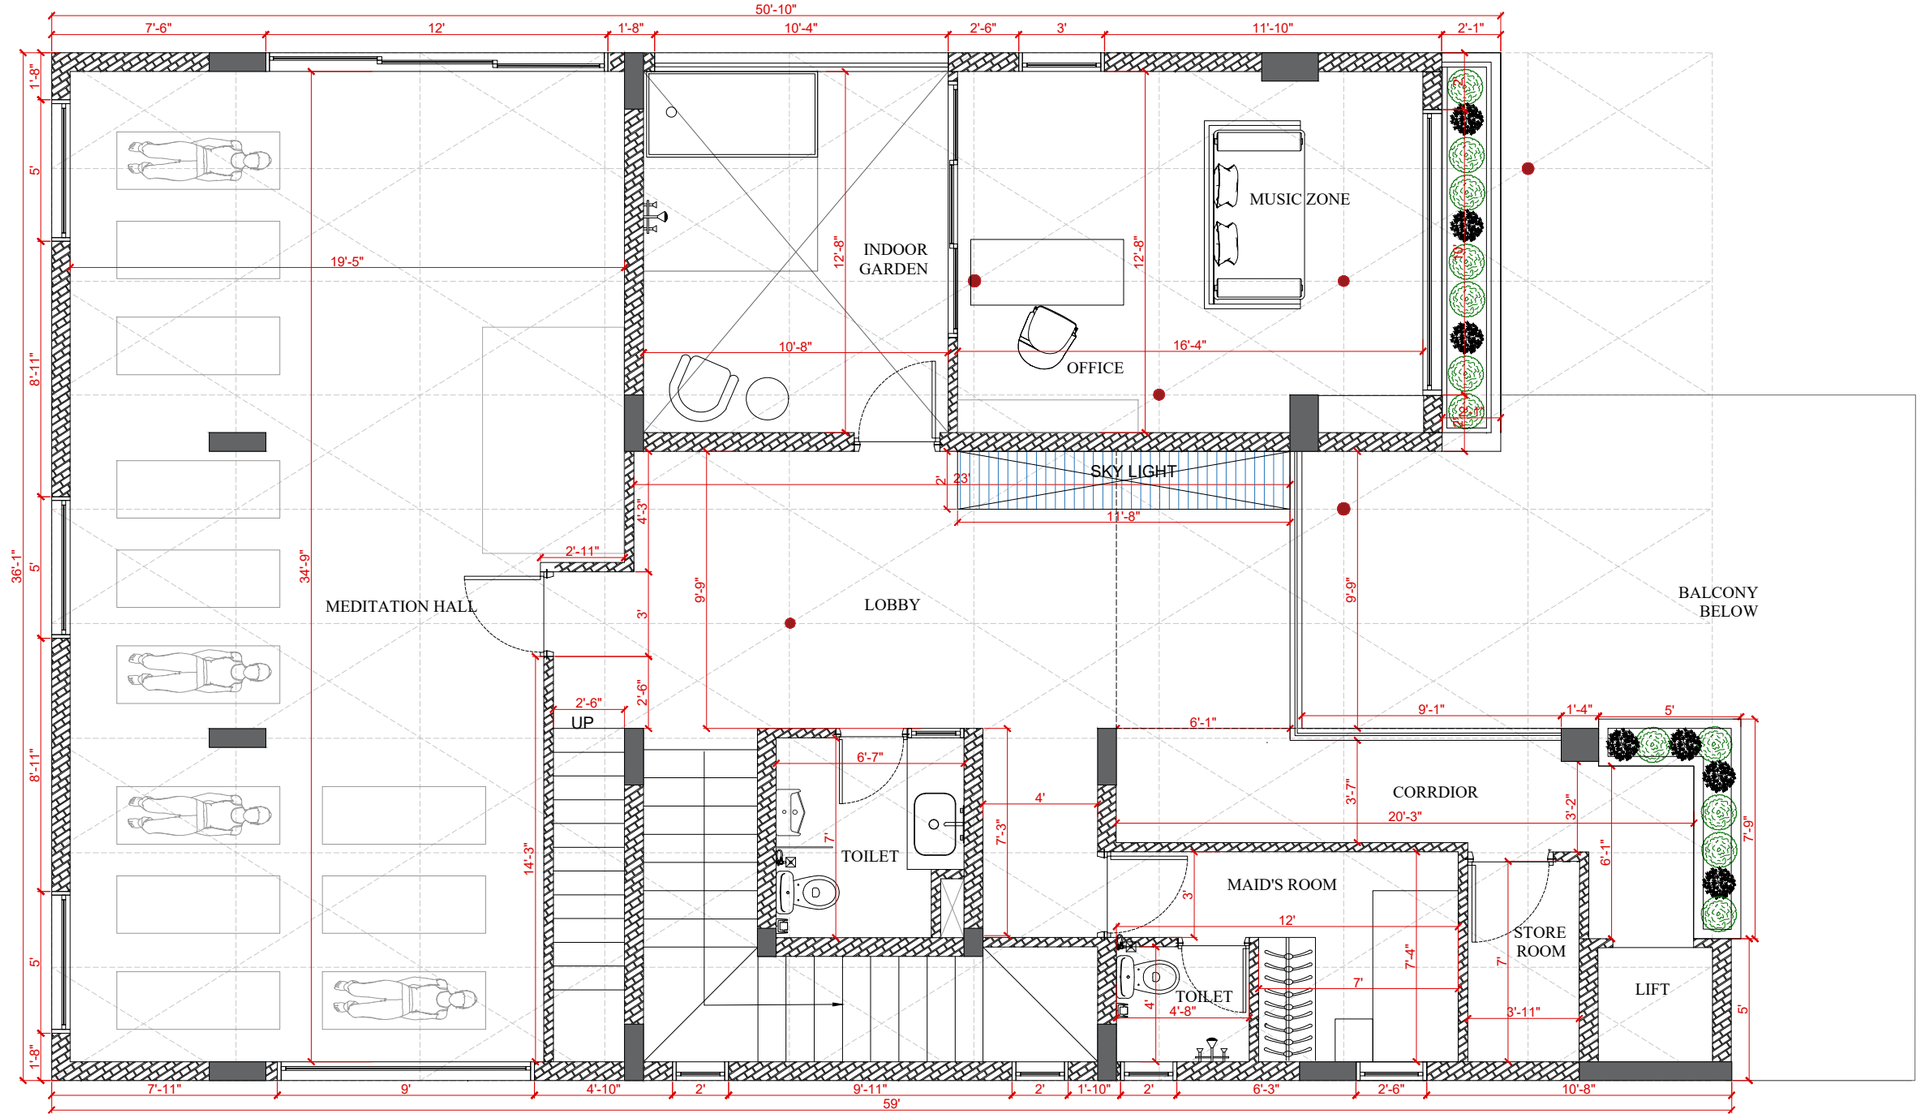

PROJECT : FLORESTA 28 — MR. MANIK'S RESIDENCE	SHEET TITLE : **SECOND FLOOR PLAN**	PARTICULARS / BY	SCALE : N.T.S.	DATE : 03-07-2026	DESIGN CONSULTANT : **ICONIC DESIGN INDIA** EAST SAPPHIRE , SECTOR - 45 NOIDA(U.P.)201301
		DRAWN :- OM	PAPER SIZE :	SHEET NO : FR-CD-F03	
		CHECKED :- SB			
		REVISION :- R5			

E:\USB Drive\DATA\ICONIC\logo.p

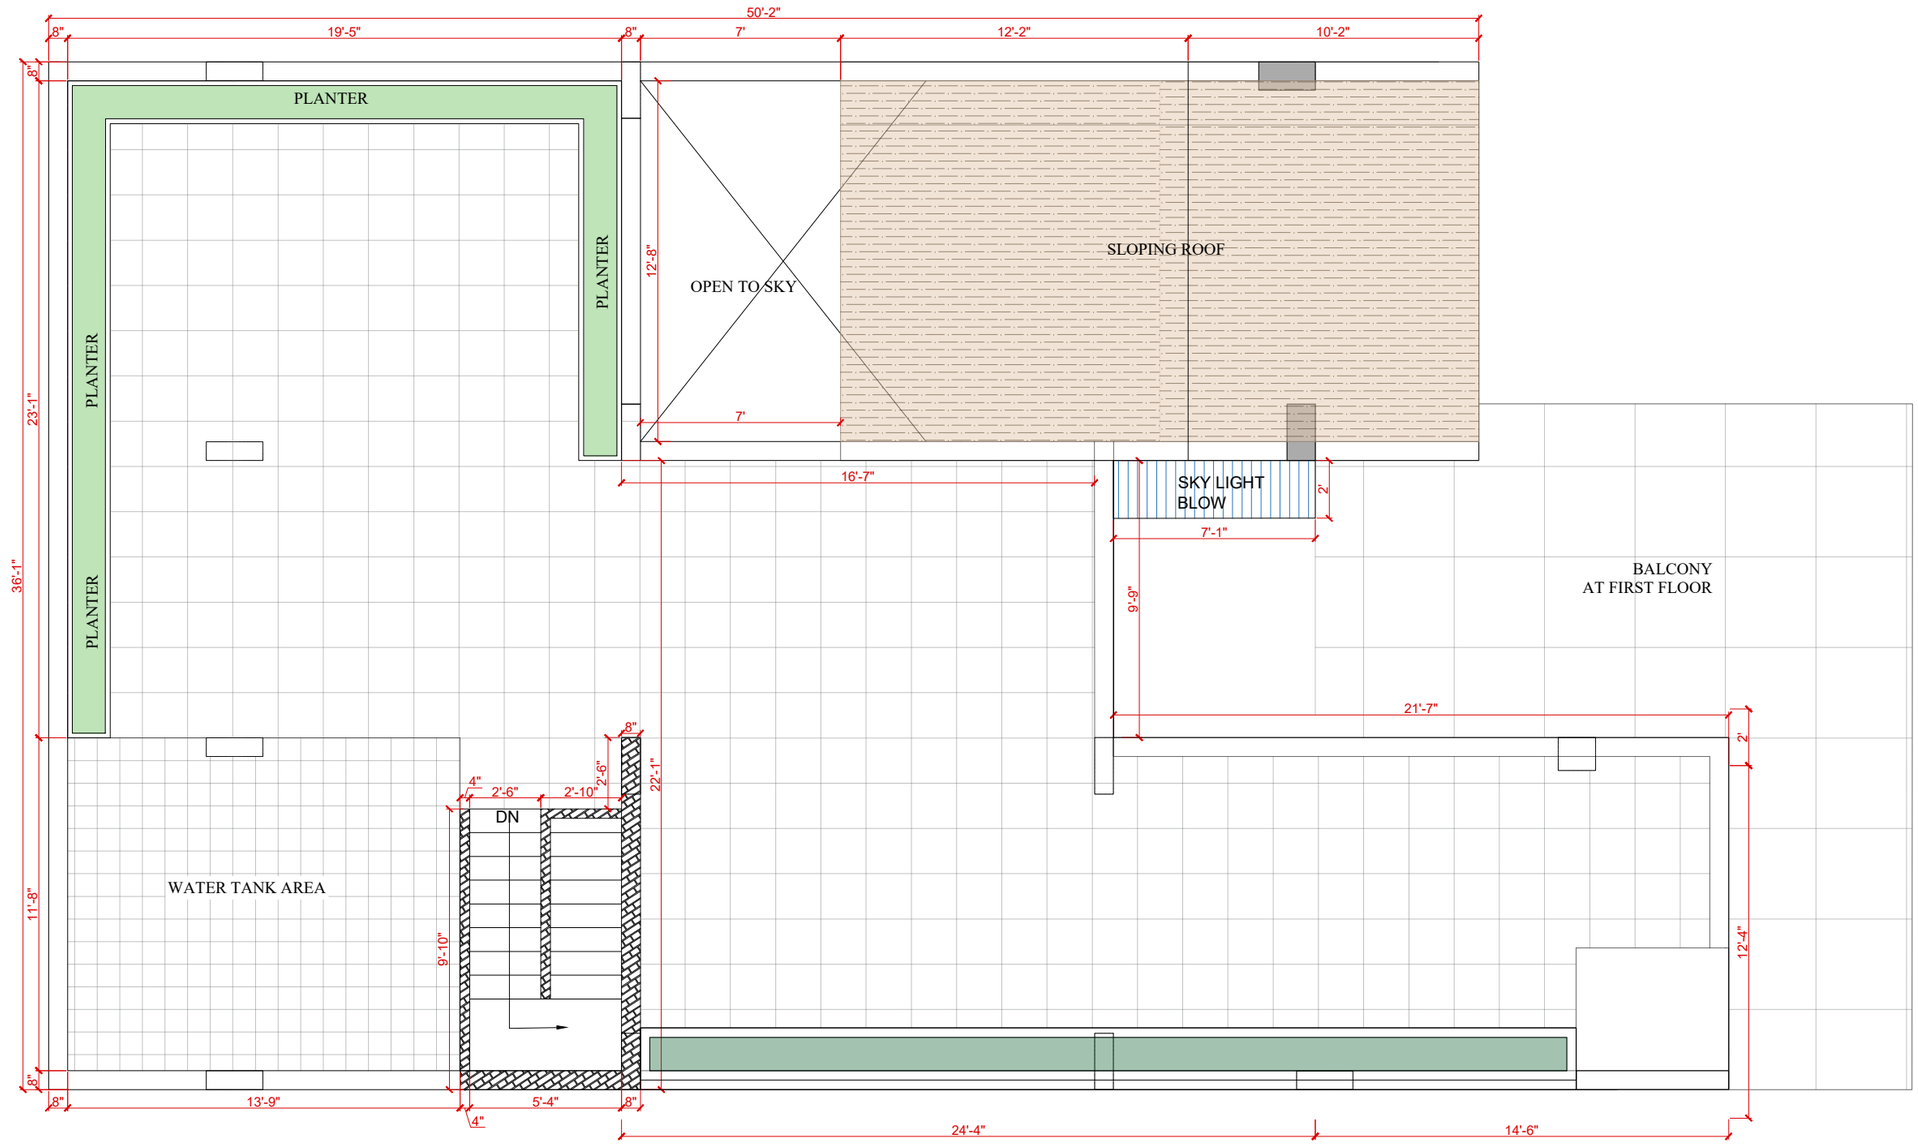

PROJECT : FLORESTA 28 — MR. MANIK'S RESIDENCE	SHEET TITLE : **TERRACE PLAN**	PARTICULARS / BY DRAWN :- OM CHECKED :- SB REVISION :- R3	SCALE : N.T.S. PAPER SIZE :	DATE : 03-07-2026 SHEET NO : FR-CD-F04	DESIGN CONSULTANT : **ICONIC DESIGN INDIA** EAST SAPPHIRE , SECTOR - 45 NOIDA(U.P.)201301

E:\USB Drive\DATA\ICONIC\logo